

اعداد المخطط العام والتفصيلي لمنطقة GOV2
متعددة الاستعمالات Downtown بالعاصمة الادارية الجديدة

كارت وصف واشترطات ومتطلبات مراجعة التصميم
القطعة رقم (MU4 - 29) بمنطقة الاستعمالات المختلطة


Downtown District - GOV2

تقع القلعة في منطقة الاستعمالات المنقطة في مشروع (Downtown - GDV2) بالتوسعة الإدارية الجديد على مساحة 1.105 هكتار تقريباً كما حدد بالشكل أدناه.




1. بحث خبزت الوصف لقطعة الأرض. يبيع إشرافه المتقوية به جزء لا يتجزأ من الأرض.
2. الالتزام بقرود انثى الذكية ومطلبات شركة العاصمة الإدارية للتنمية العمرانية.
3. الالتزام بقرود الألوان والإشرافات المعمارية للمباني الخاصة بالعاصمة الإدارية.
4. معامل الأمان (FAR) والتنمية انثى تحسب من قرود الملكية لقطعة الأرض.
5. يجب تطوير البنى التحتية بالمدينة المخصصة لها كما هو موضح بخريطة القطعة المرفقة حتى أن يكون ارتفاع البنايات (الرصني + أول) فقط.
6. الاستخدام المتكامل لمخطط (باري / سكني / تجاري /) حيث التوزيع السليم من ممتص : على أن يكون ملائماً لعدد أماكن الإقطار المطلوب توافرها و استيعاب شبكة المرافق.
7. يجب دراسة كثير مدعى المشروع على المدى المجاورة من حيث دراسات نفق الرياح (wind tunnel) ومركز المباني (Staggering).

- 3-6-2025

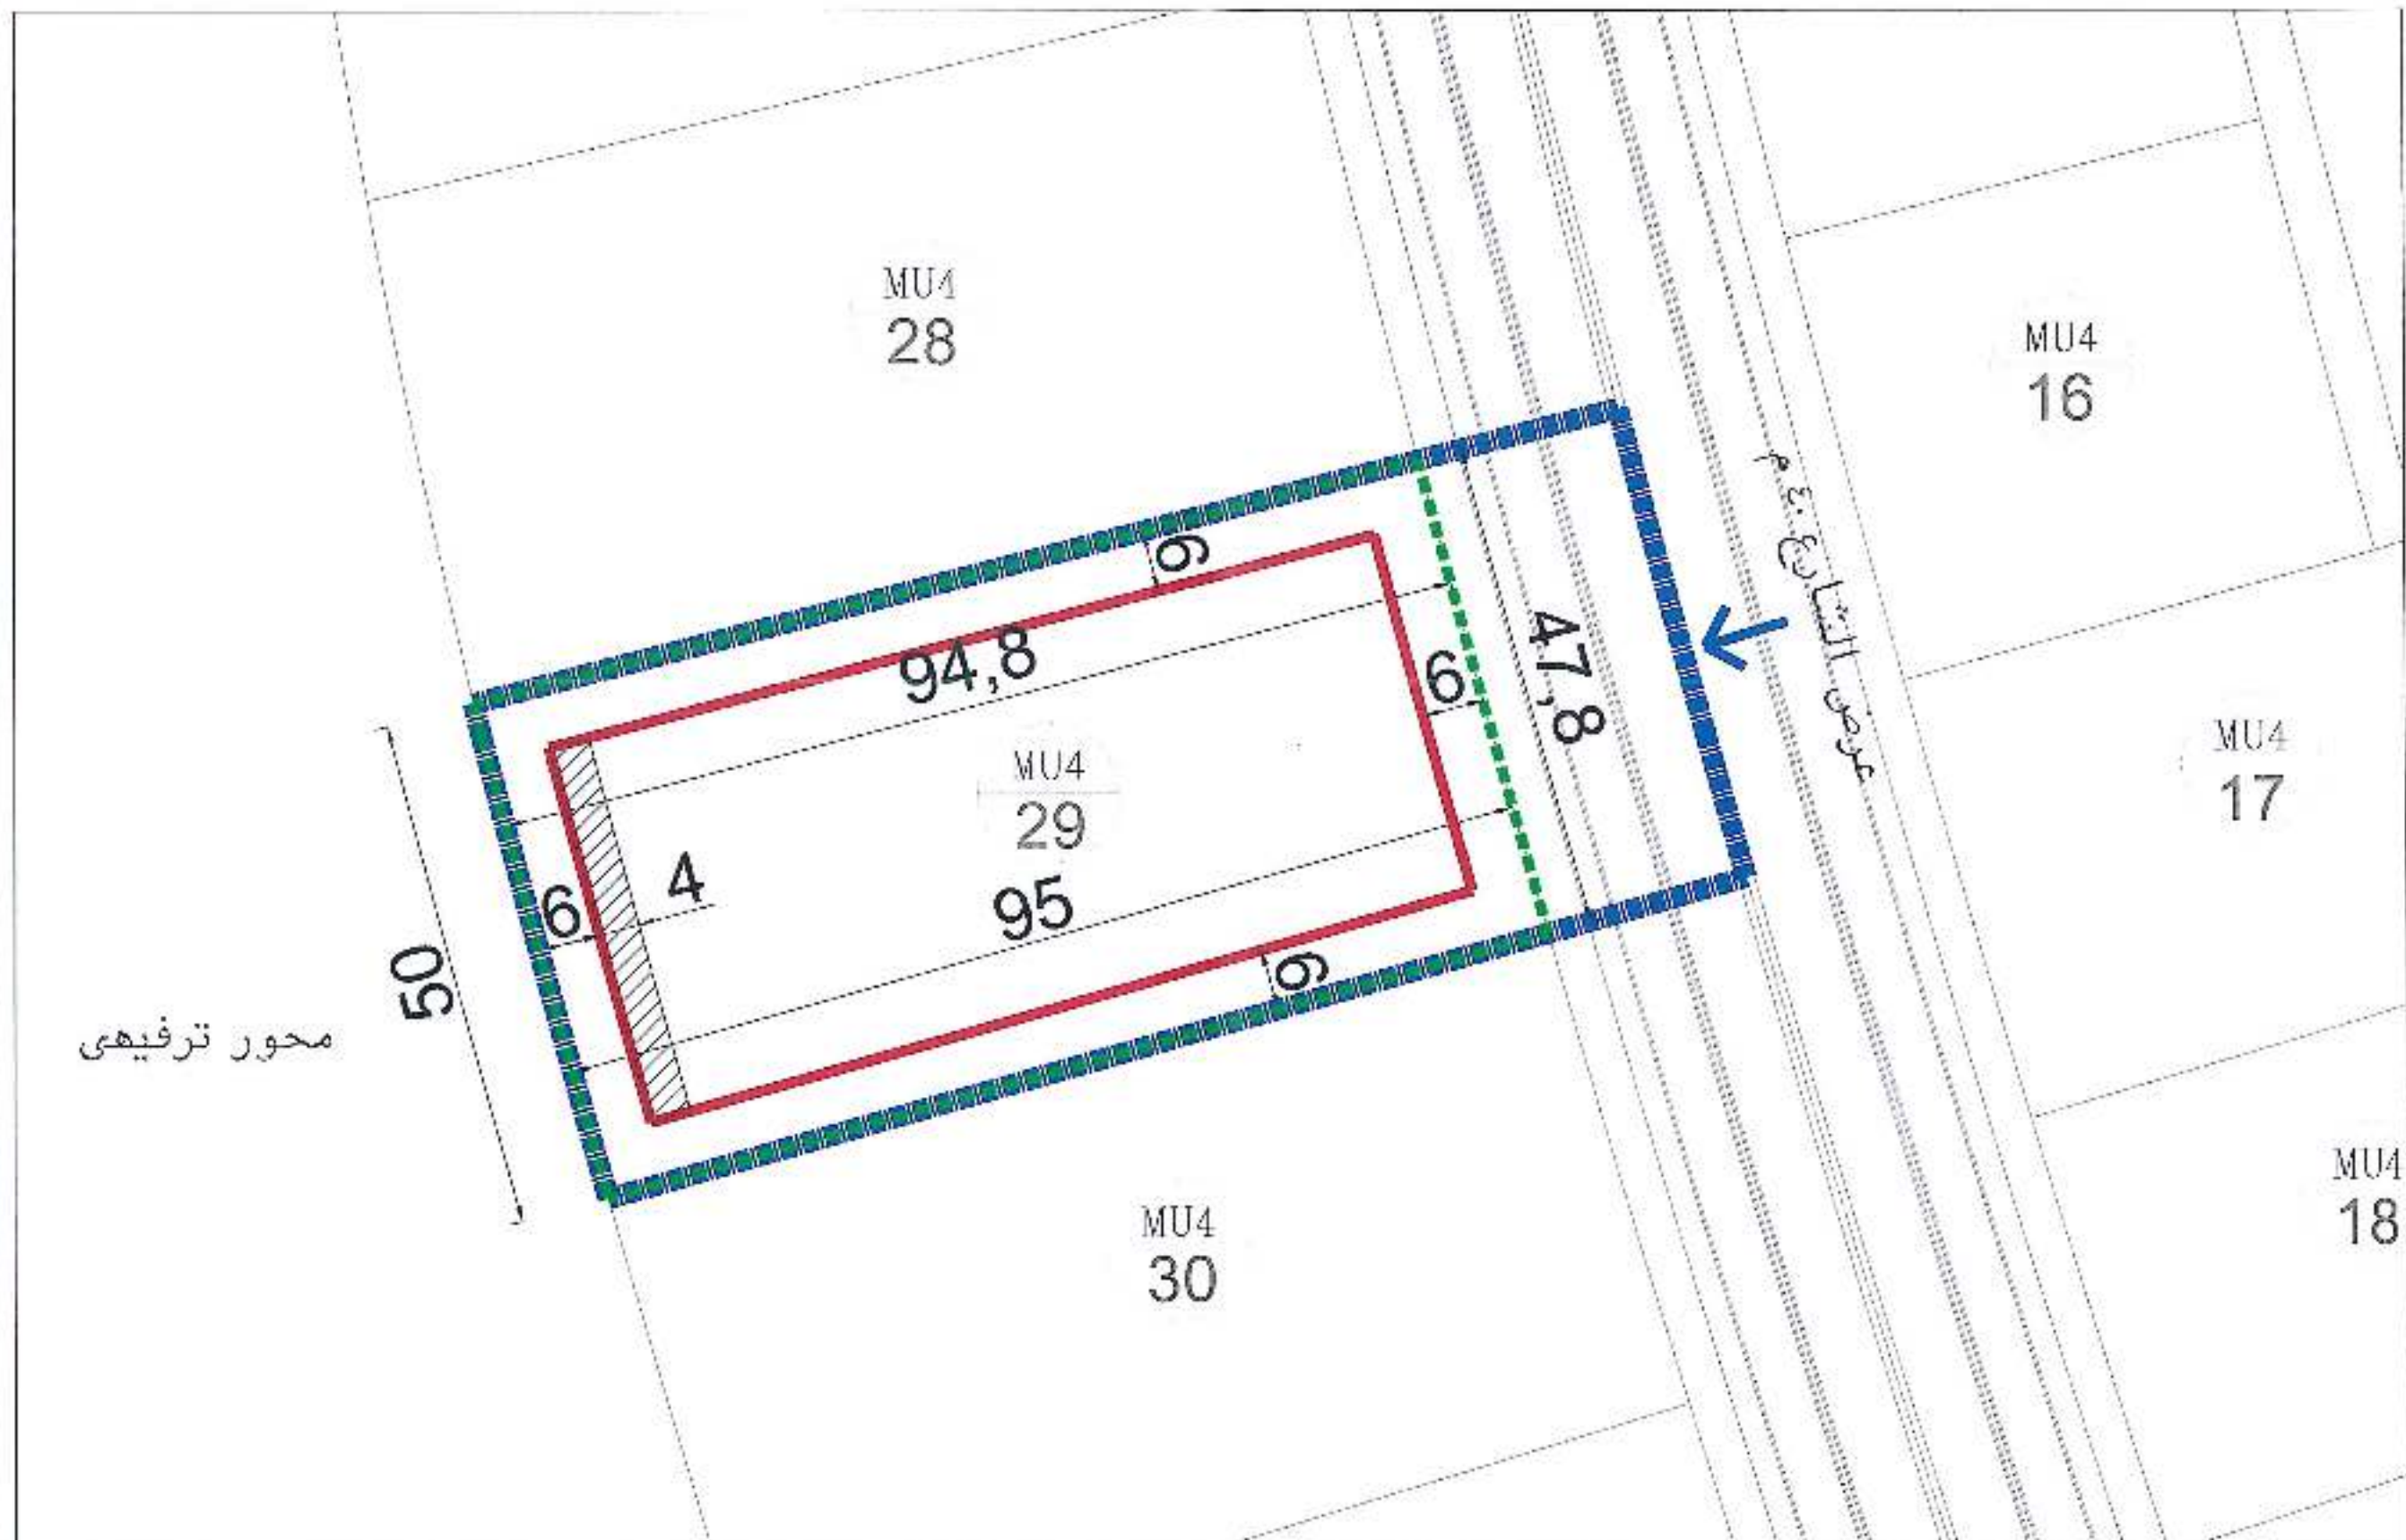

اسم المخطط اعداد المخطط العام و التفسير لمشكلة GOV2 معدة الاستشارات Downtown بالعاصمة الادارية الجديدة	المالك شركة العاصمة الادارية للتقنية الادارية	المستشار العام ARCHITECT مهندسين معماريين 100 شارع النور القاهرة 11511	اسم الوحدة القطعة (29-MU4-IDT) موقع الاستشارات المنطقة	التاريخ يوليو 2025	المساحة الكلية 00947009 م ² حدود الملكية 2629.8979 م ²	حدود الارضادات 2-58,7738 م ² منطقة يلتزم فيها بانشاء البنايات المعمارية بمساحة 101 م ²	→ واجبات داخل ومخارج المشروع
--	--	--	--	-----------------------	---	---	------------------------------

MU4 - 29		
احداثيات حدود المساحة الكلية		
ID	X	Y
1	686474.0502	810113.4738
2	686363.4811	810082.2982
3	686357.2233	810104.9599
4	686350.5287	810130.5895
5	686461.6954	810159.1962
احداثيات حدود الملكية		
ID	X	Y
1	686442.3265	810154.2119
2	686448.4298	810131.0929
3	686454.8008	810108.0463
4	686363.4811	810082.2982
5	686357.2233	810104.9599
6	686350.5287	810130.5895
احداثيات حدود الارتداد		
ID	X	Y
1	686438.022	810146.9088
2	686447.4021	810112.1941
3	686367.6357	810089.7035
4	686357.7799	810126.26

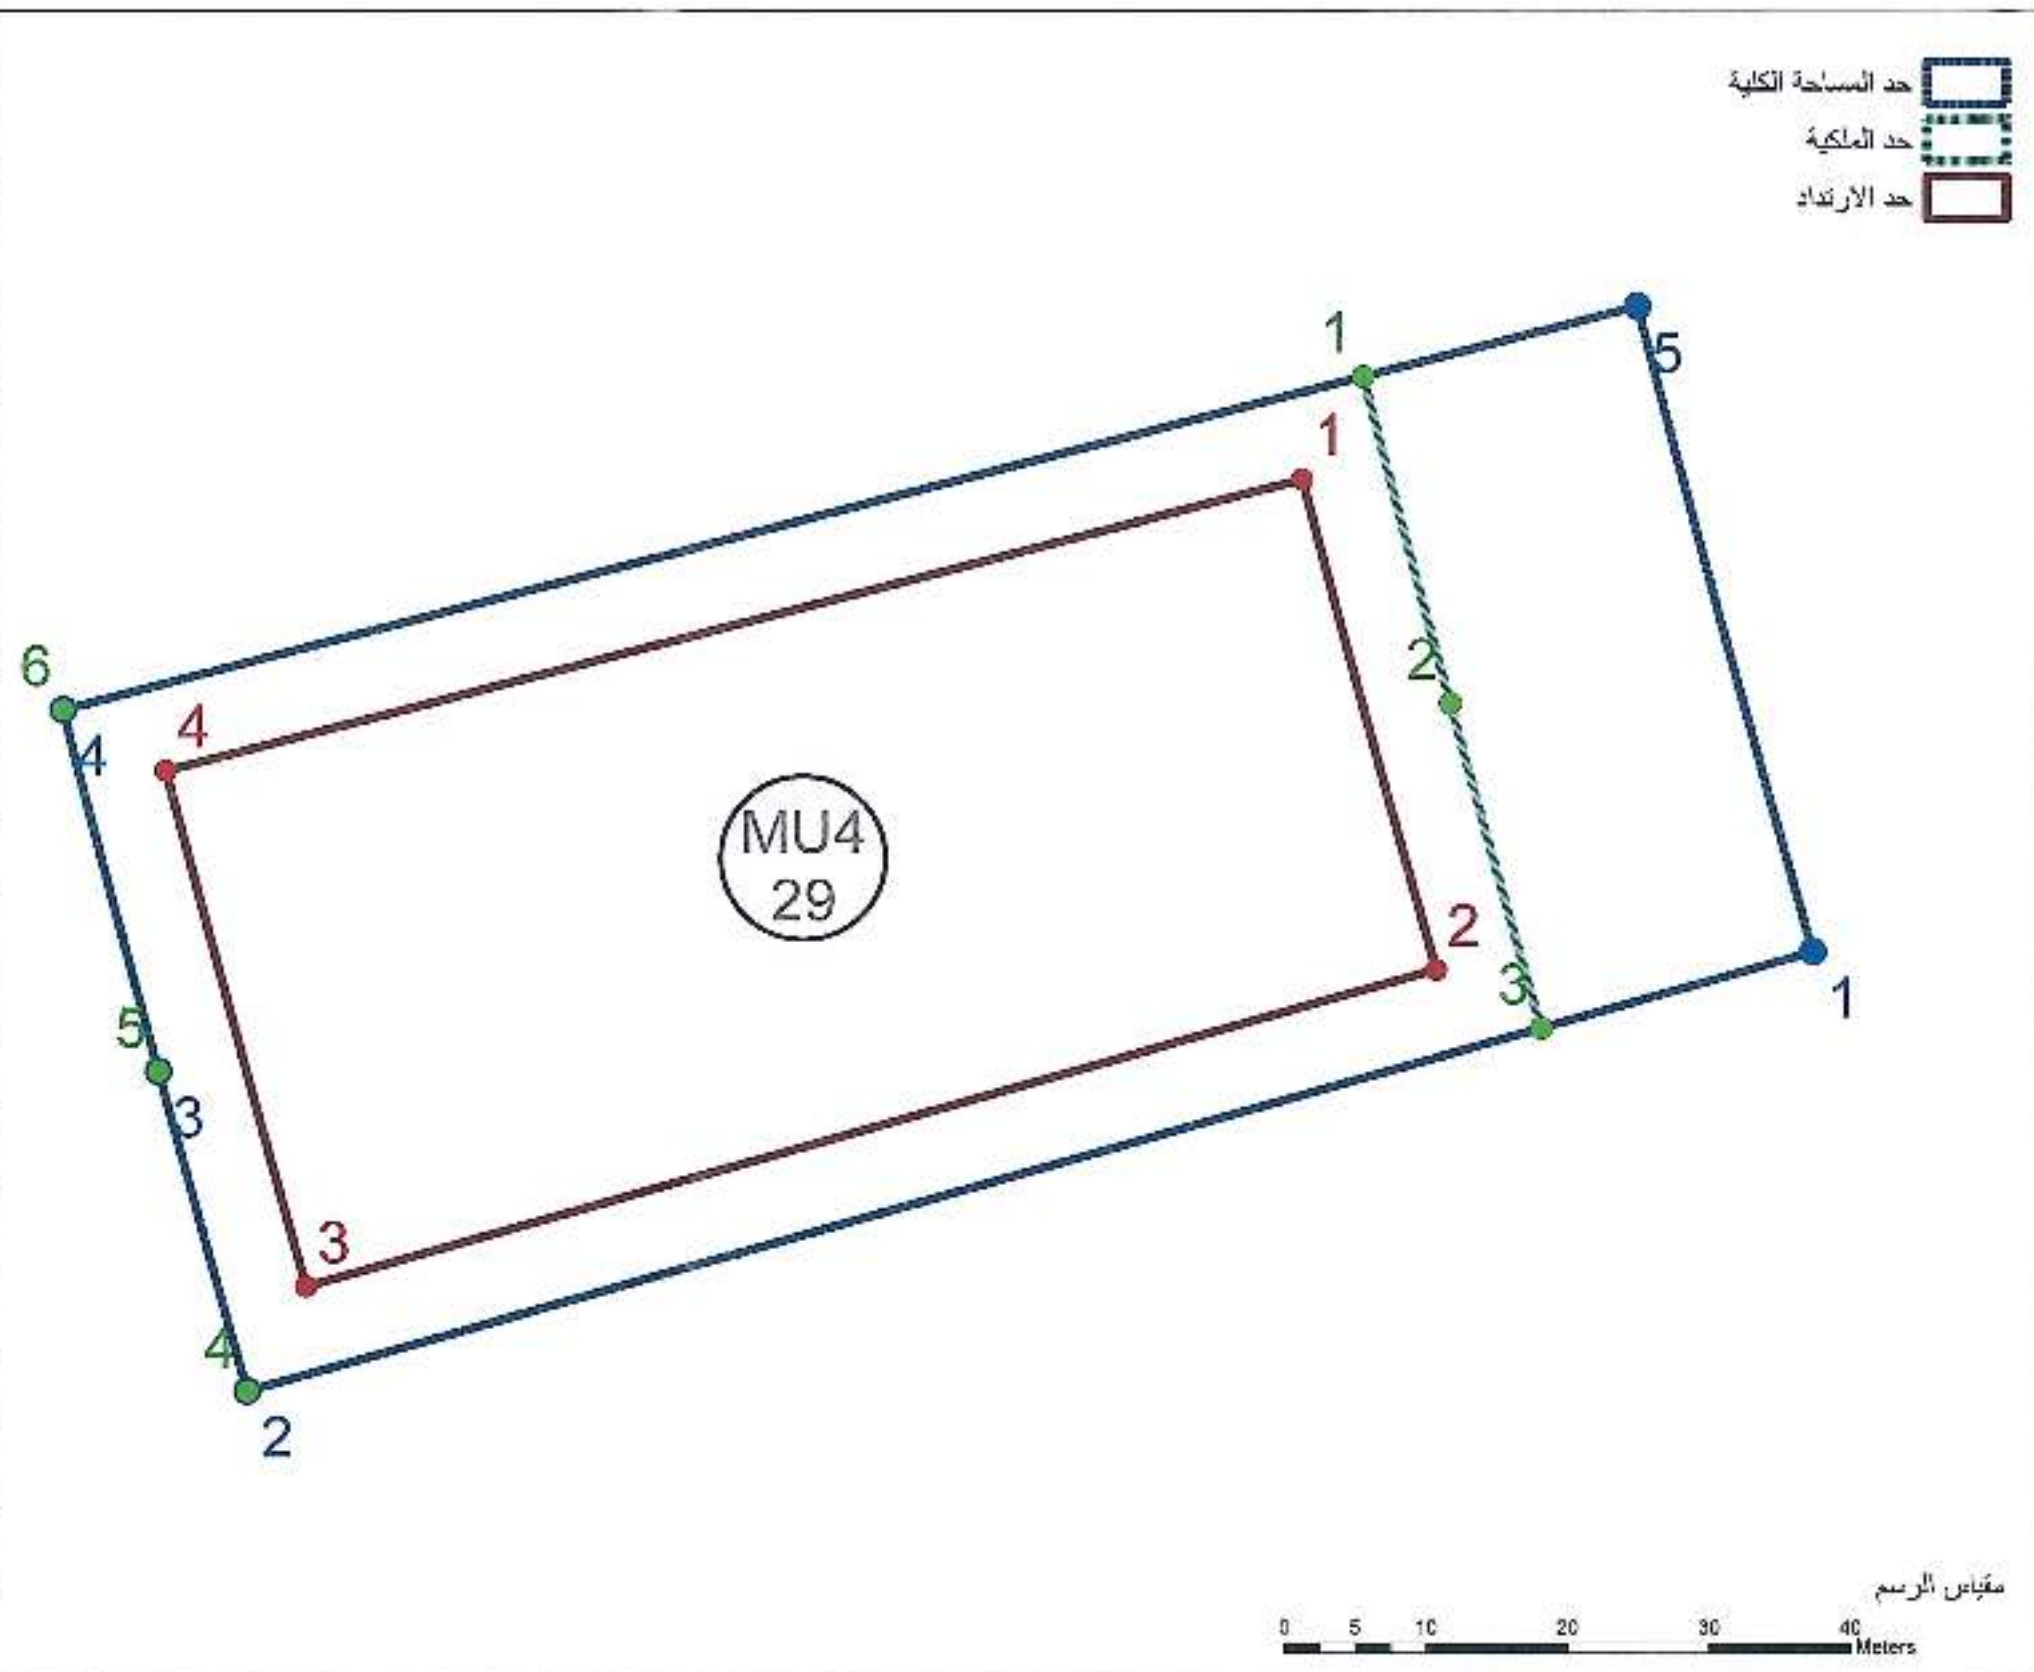

الإحداثيات المستخدمة على نظام الإحداثيات المسوية لمنطقة المزارع الأحمر
المرجع الجيوديسي المستخدم هو المعيار العالمي فيلبرت 1906
الانحناء المستخدم هو نظام مركزية الإسقاط العرضي
The Coordinates used on the Egyptian Coordinate system,
the red belt zone. The geodesic reference used is Helmert
1906 Global ellipsoid. Projection used is the Egyptian
transverse Mercator system.

التاريخ
يوليو 2025

اسم الوحدة
إحداثيات القطعة (DT/ MU4 - 29)
في منطقة الاستعمالات المختلطة

الاستشاري العام



المالك



شركة العاصمة الإدارية للتنمية العمرانية

اسم المشروع

إعداد المخطط العام والتفصيلي لمنطقة GOV2
متعددة الاستعمالات Downtown بالعاصمة
الإدارية الجديدة

